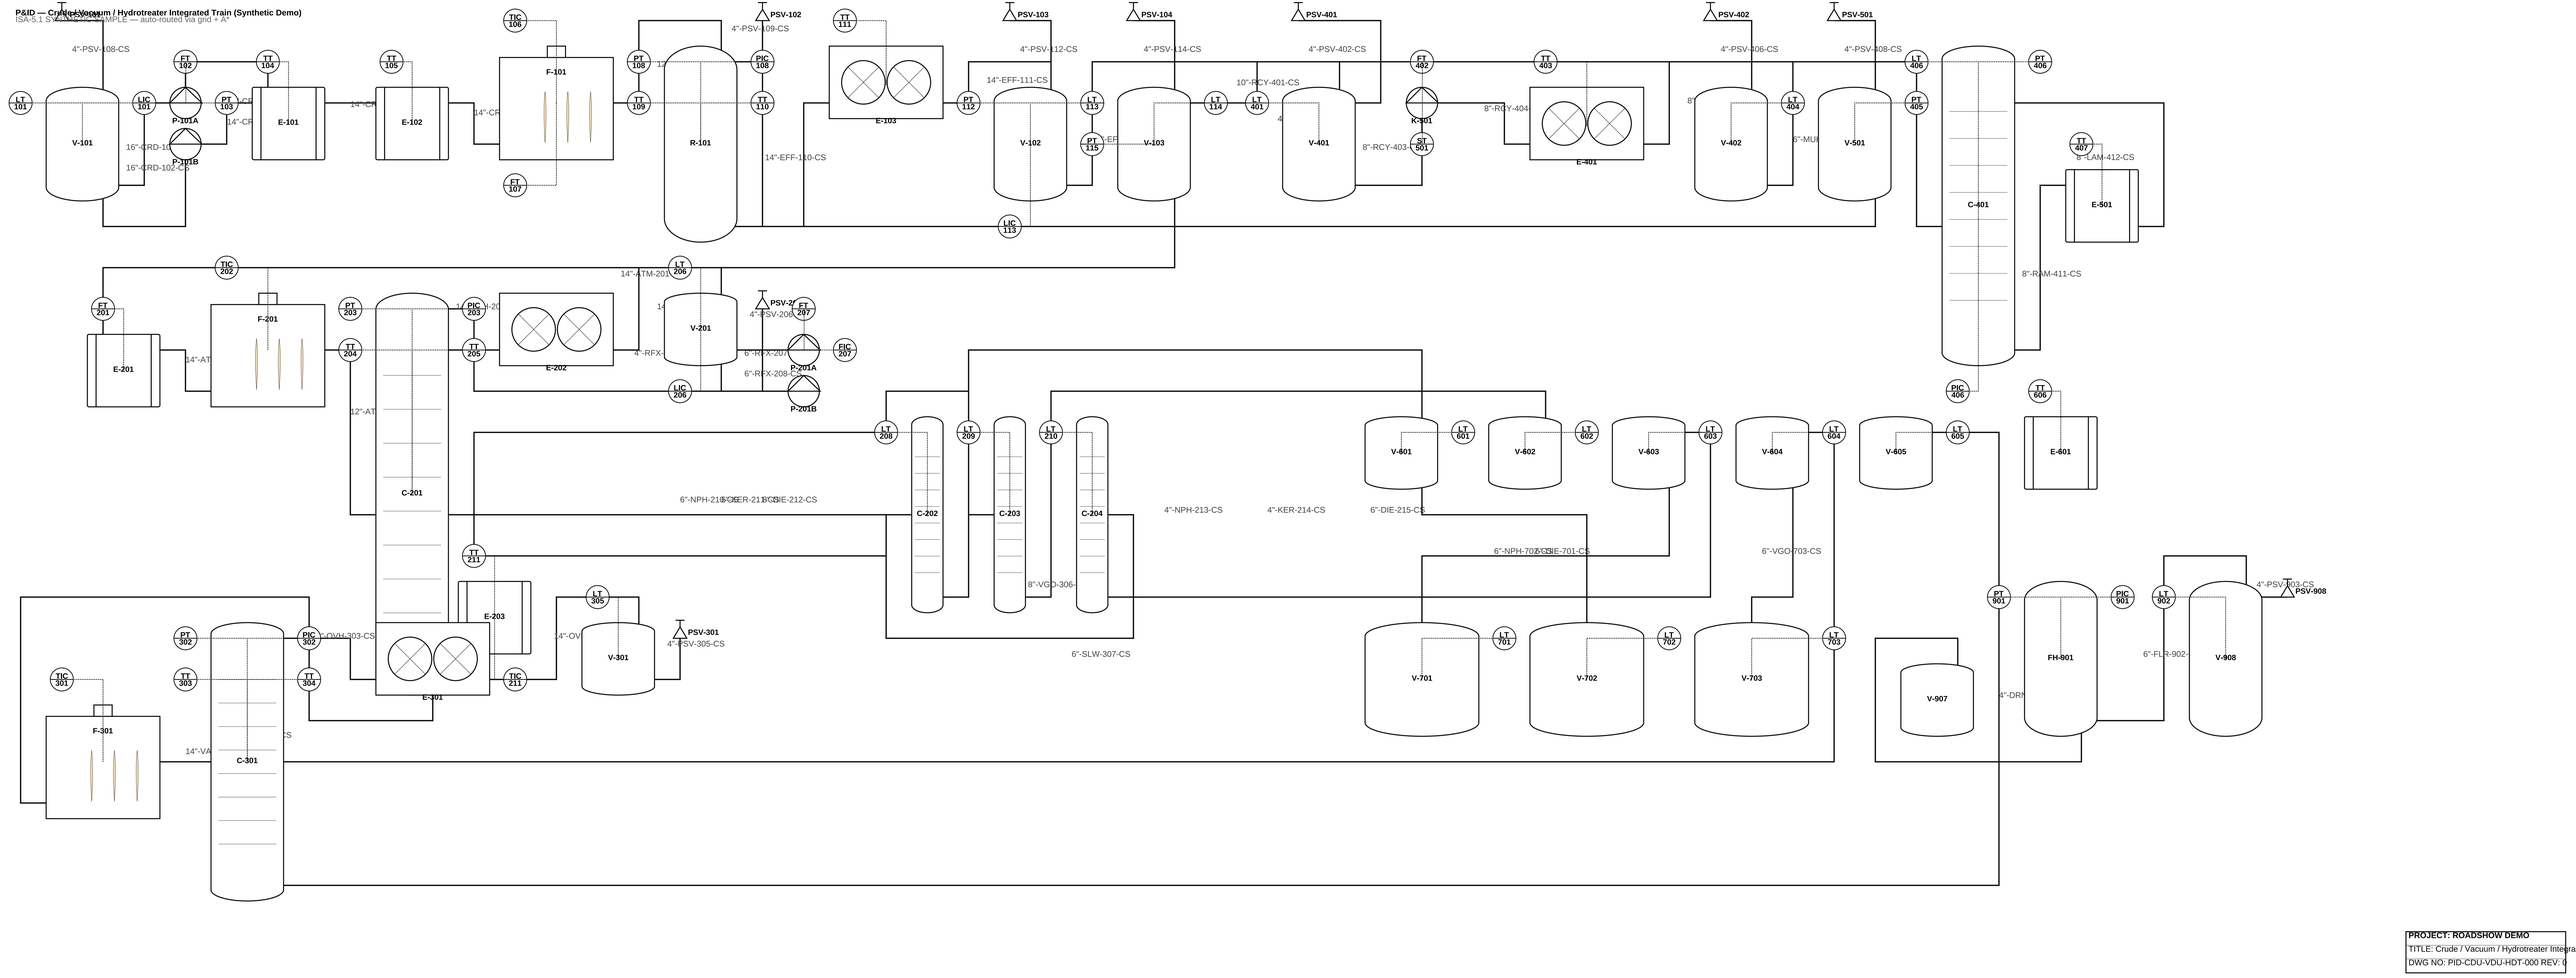

P&ID — Crude / Vacuum / Hydrotreater Integrated Train (Synthetic Demo)

ISA-5.1 SYNTHETIC SAMPLE — auto-routed via grid + A*

PSV-101
4"-PSV-108-CS
LT 101
V-101
LIC 101
FT 102
P-101A
P-101B
16"-CRD-10
16"-CRD-102-CS
PT 103
14"-CR
TT 104
E-101
14"-CR
TT 105
E-102
14"-CR
TIC 106
F-101
FT 107
PT 108
TT 109
R-101
PSV-102
4"-PSV-109-CS
PIC 108
TT 110
14"-EFF-110-CS
TT 111
E-103
PT 112
PSV-103
4"-PSV-112-CS
14"-EFF-111-CS
V-102
LIC 113
LT 113
PT 115
"-EF
PSV-104
4"-PSV-114-CS
V-103
LT 114
LT 401
10"-RCY-401-CS
PSV-401
4"-PSV-402-CS
V-401
FT 402
K-501
ST 501
8"-RCY-403-
8"-RCY-404
TT 403
E-401
PSV-402
4"-PSV-406-CS
V-402
LT 404
6"-MUI
PSV-501
4"-PSV-408-CS
V-501
LT 406
PT 405
C-401
PT 406
TT 407
8"-LAM-412-CS
E-501
8"-RAM-411-CS
PIC 406
TIC 202
FT 201
E-201
14"-AT
F-201
PT 203
TT 204
12"-AT
C-201
PIC 203
TT 205
14"-ATM-201
E-202
4"-RFX-
LT 206
V-201
LIC 206
PSV-2
4"-PSV-206
FT 207
6"-RFX-207
6"-RFX-208-CS
P-201A
P-201B
FIC 207
LT 208
C-202
LT 209
C-203
LT 210
C-204
6"-NPH-210-CS
6"-KER-211-CS
8"-DIE-212-CS
4"-NPH-213-CS
4"-KER-214-CS
6"-DIE-215-CS
8"-VGO-306-
6"-SLW-307-CS
V-601
LT 601
V-602
LT 602
V-603
LT 603
V-604
LT 604
V-605
LT 605
TT 606
E-601
6"-NPH-702-CS
6"-DIE-701-CS
6"-VGO-703-CS
V-701
LT 701
V-702
LT 702
V-703
LT 703
TT 211
E-203
LT 305
14"-OV
V-301
PSV-301
4"-PSV-305-CS
PT 302
PIC 302
"-OVH-303-CS
TIC 301
TT 303
TT 304
E-301
TIC 211
F-301
14"-VA
C-301
CS
PT 901
FH-901
PIC 901
LT 902
V-908
PSV-908
4"-PSV-903-CS
6"-FLR-902-
V-907
4"-DRN

PROJECT: ROADSHOW DEMO

TITLE: Crude / Vacuum / Hydrotreater Integra

DWG NO: PID-CDU-VDU-HDT-000 REV: 0